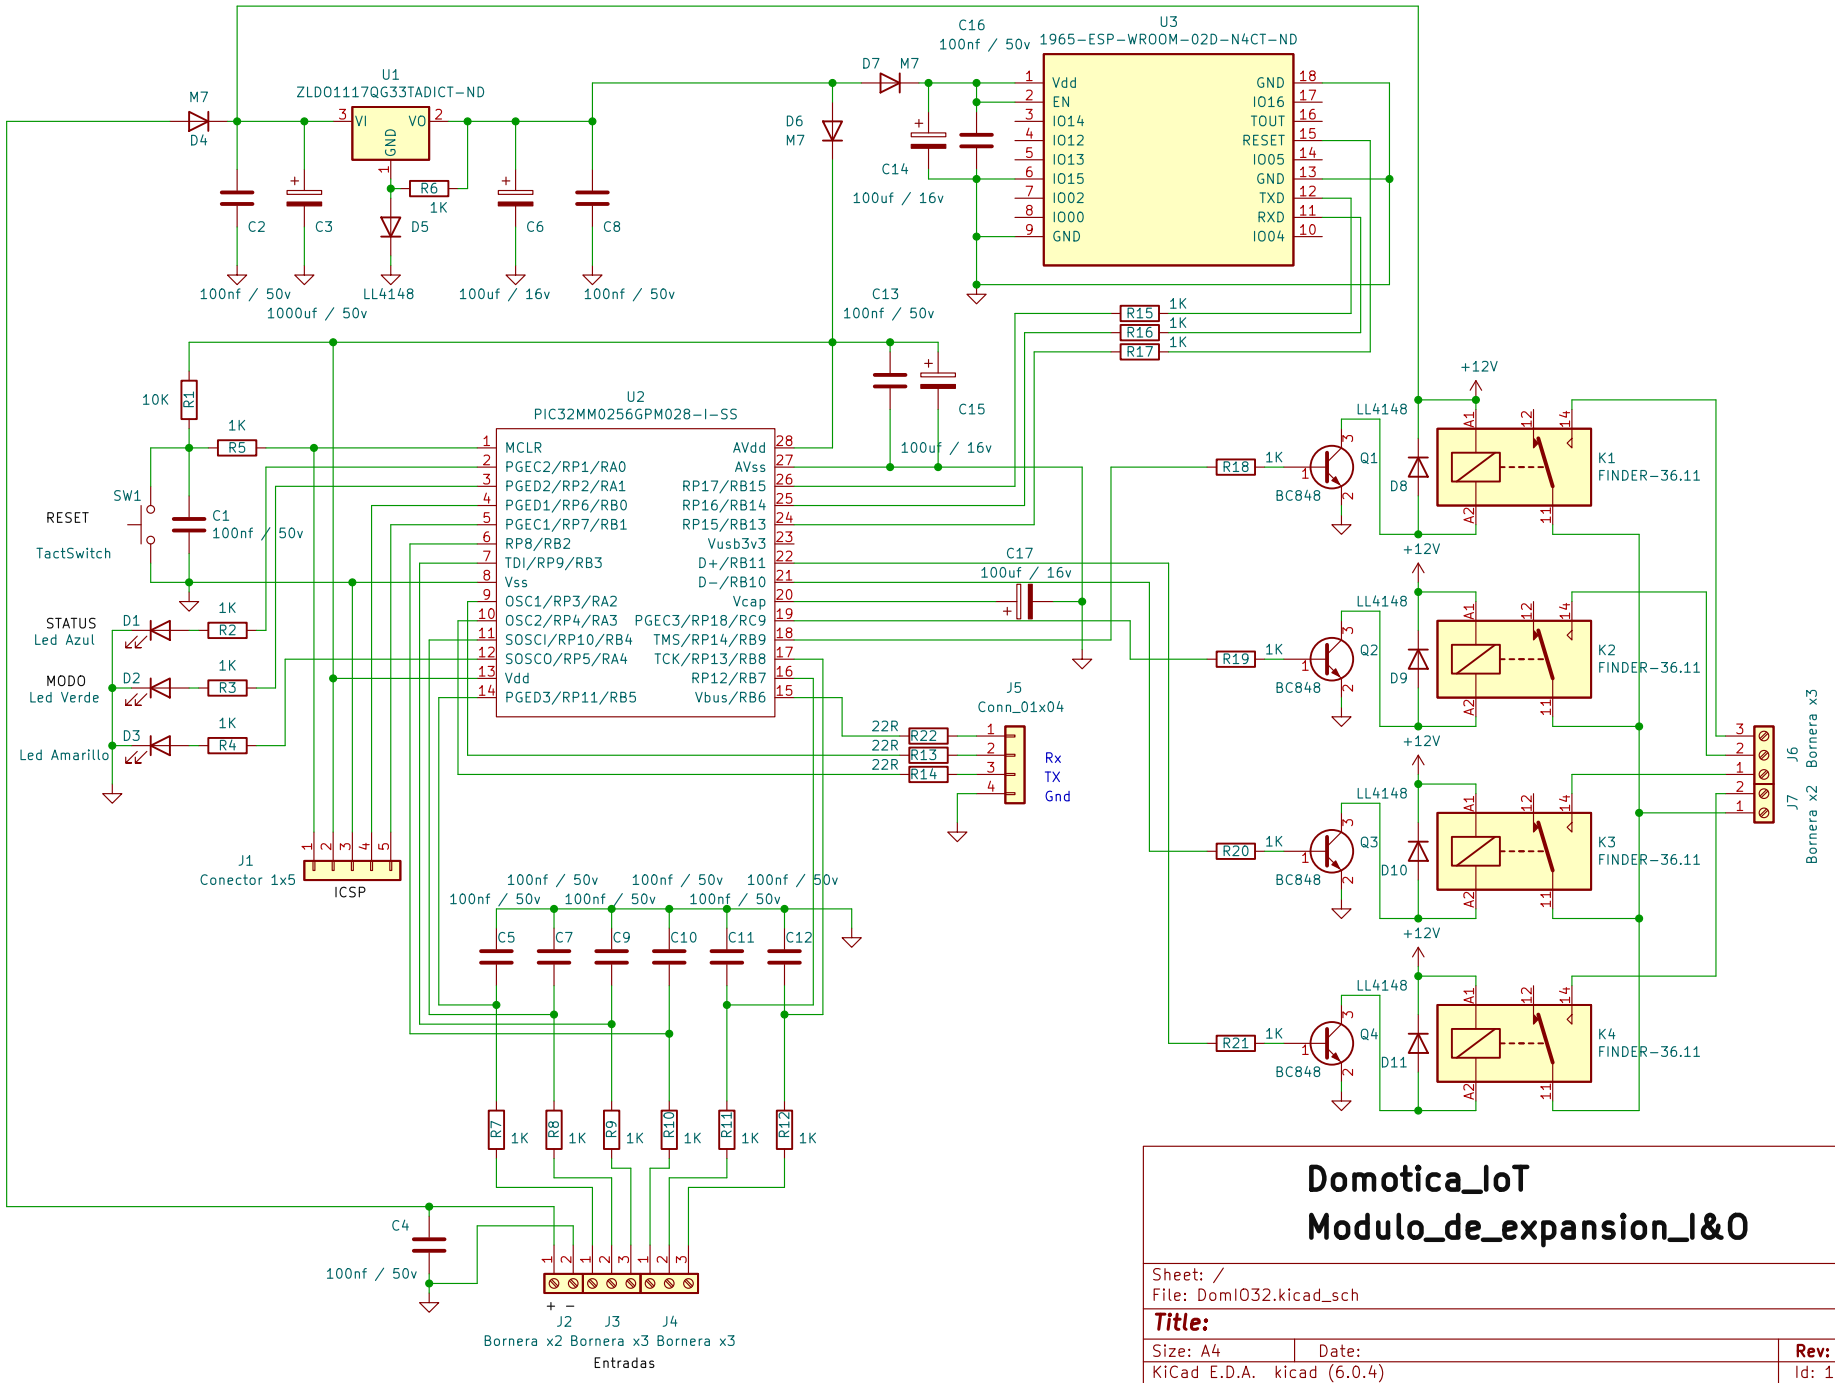

U1
ZLDO1117QG33TADICT-ND
U3
1965-ESP-WROOM-02D-N4CT-ND
U2
PIC32MM0256GPM028-I-SS
M7
D4
D6
M7
D7
M7
C16
100nf / 50v
C14
100uf / 16v
C2
100nf / 50v
C3
1000uf / 50v
C6
100uf / 16v
C8
100nf / 50v
R6
1K
D5
LL4148
C13
100nf / 50v
C15
100uf / 16v
C17
100uf / 16v
R15
R16
R17
1K
10K
R1
R5
SW1
RESET
TactSwitch
C1
100nf / 50v
STATUS
Led Azul
D1
R2
MODO
Led Verde
D2
R3
Led Amarillo
D3
R4
J1
Conector 1x5
ICSP
J5
Conn_01x04
Rx
TX
Gnd
R22
R13
R14
22R
R18
R19
R20
R21
BC848
Q1
Q2
Q3
Q4
D8
D9
D10
D11
+12V
LL4148
K1
K2
K3
K4
FINDER-36.11
J6
J7
Bornera x3
Bornera x2
C5
C7
C9
C10
C11
C12
100nf / 50v
R7
R8
R9
R10
R11
R12
C4
100nf / 50v
J2
J3
J4
Bornera x2
Bornera x3
Bornera x3
Entradas
Domotica_IoT
Modulo_de_expansion_I&O
Sheet: /
File: DomIO32.kicad_sch
Title:
Size: A4
Date:
Rev:
KiCad E.D.A. kicad (6.0.4)
Id: 1/1